






EMPOWERING FUTURE

CLIENT	MECWIN TECHNOLOGIES INDIA PVT.LTD.
ADDRESS	-----
PROJECT	300HP Submersible Pump for Refinery
JOB NO.	2025/15

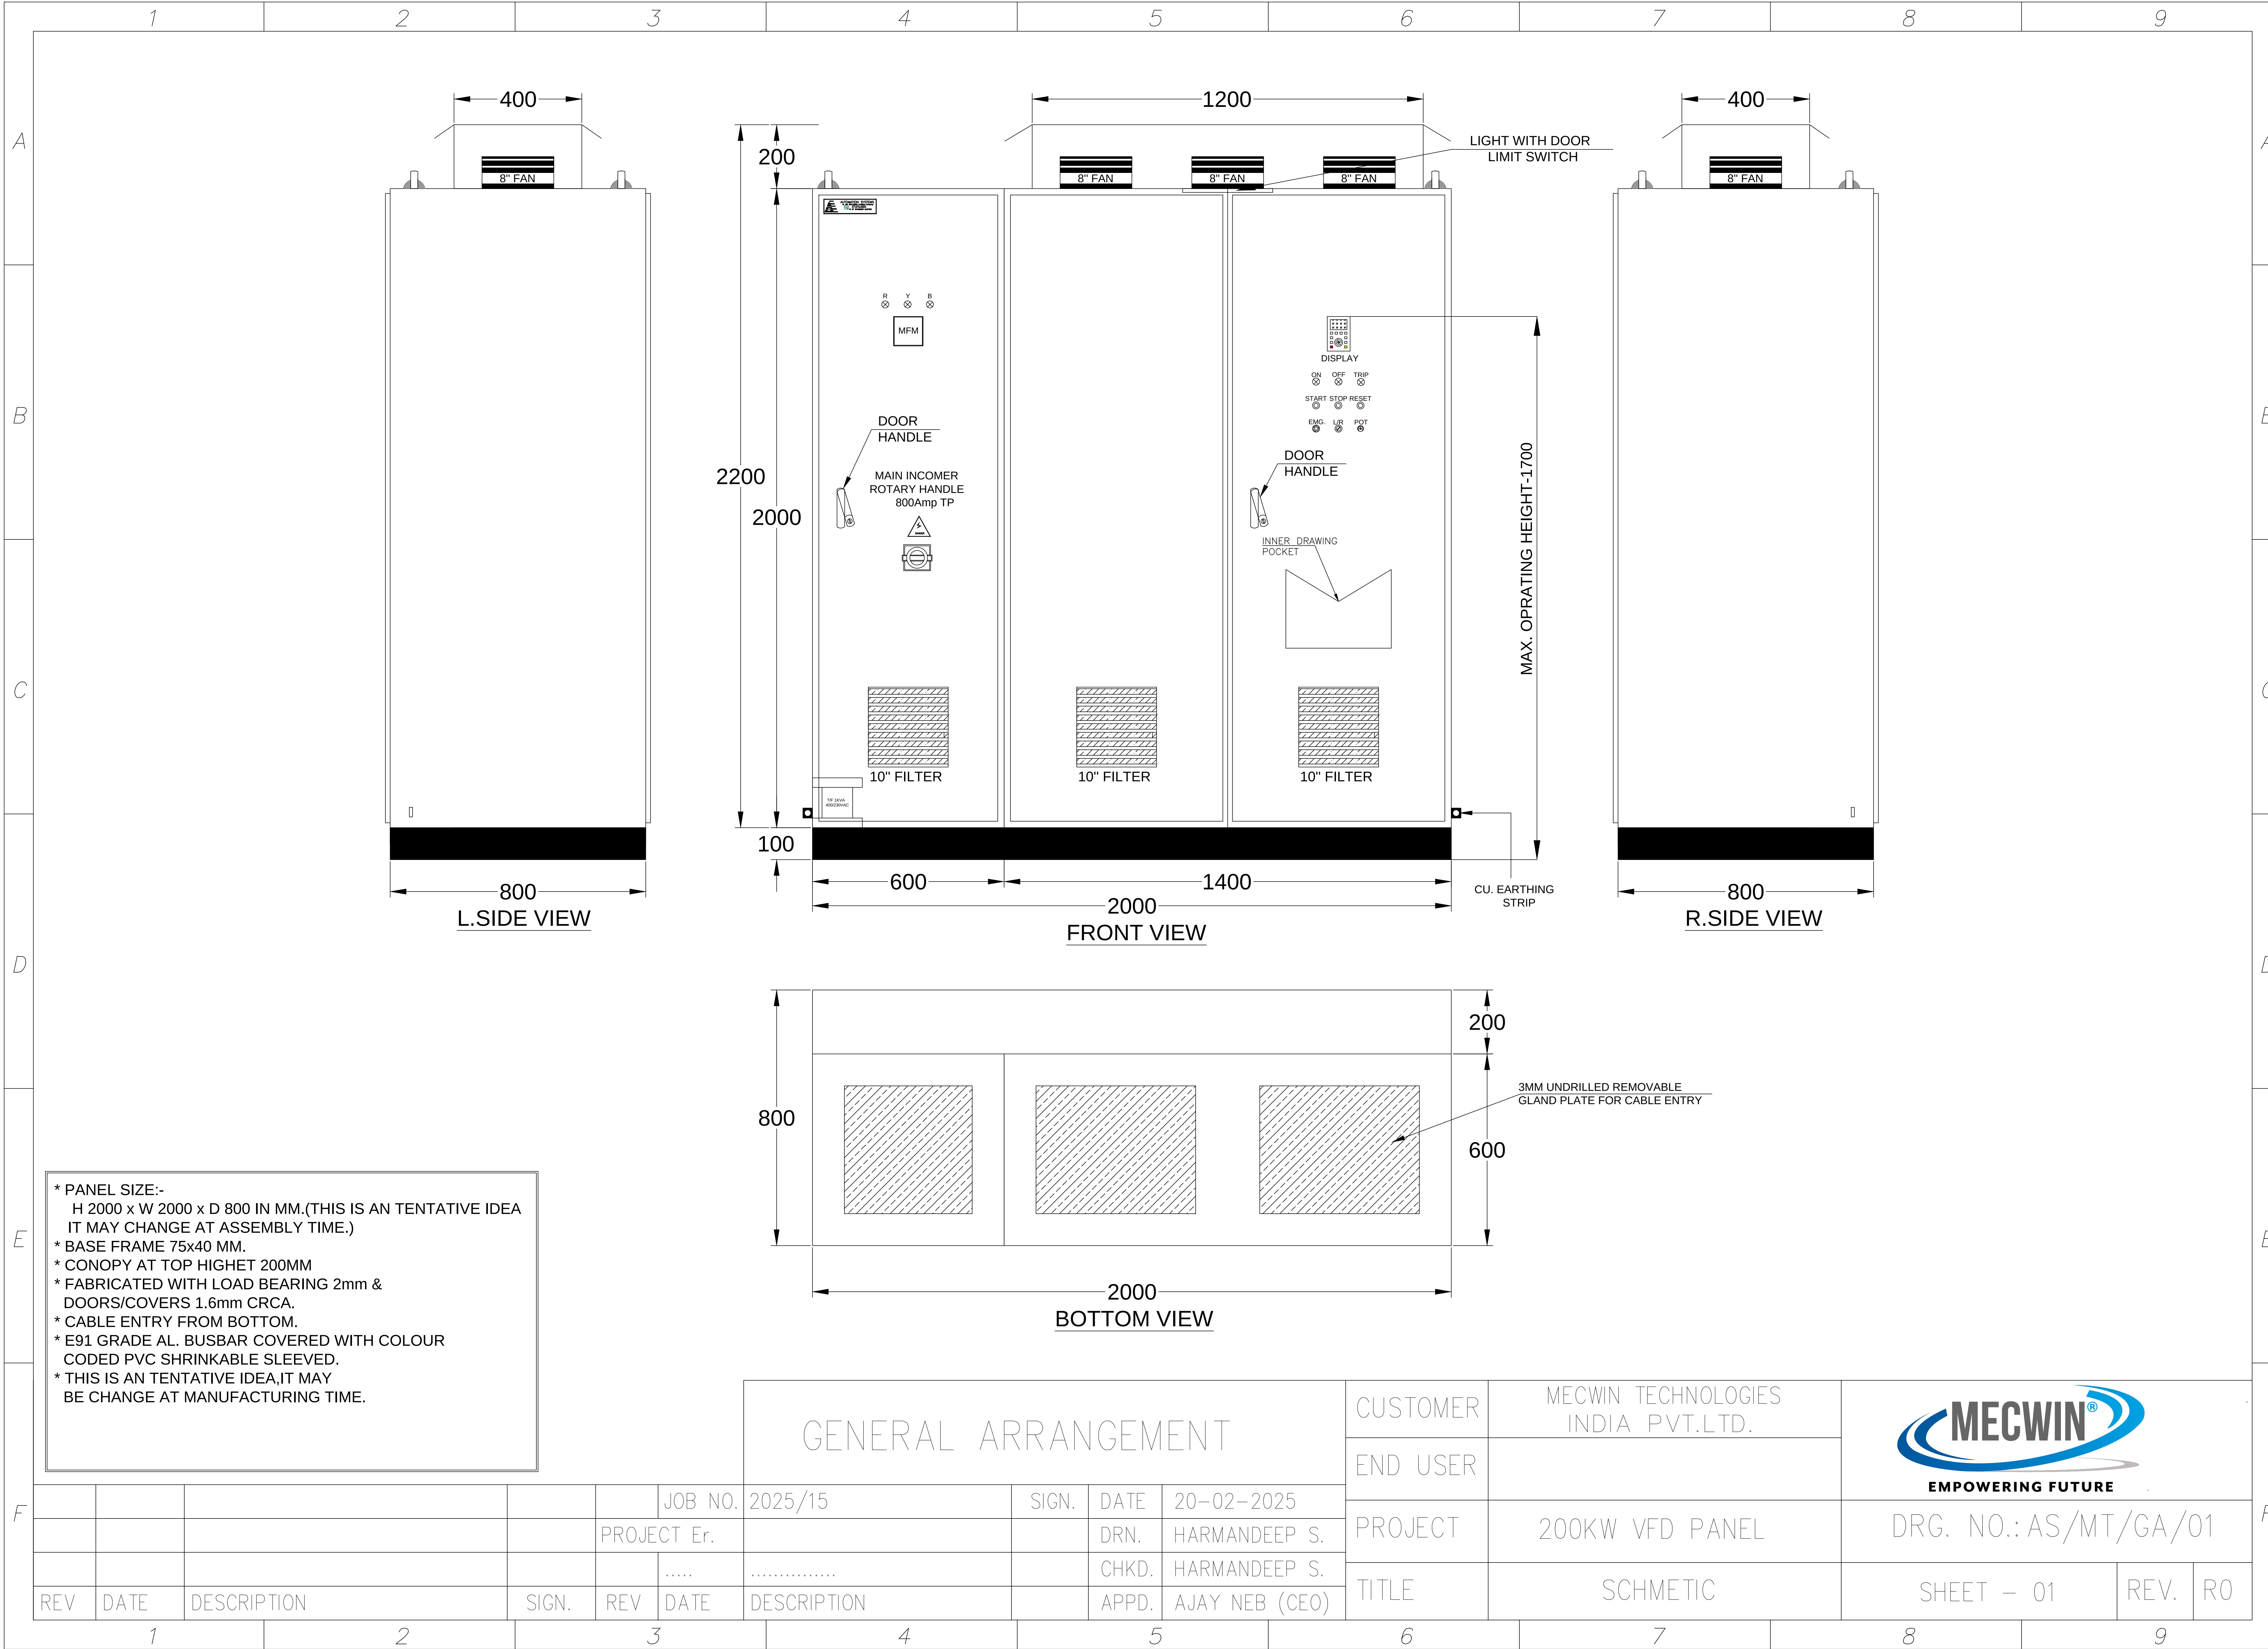

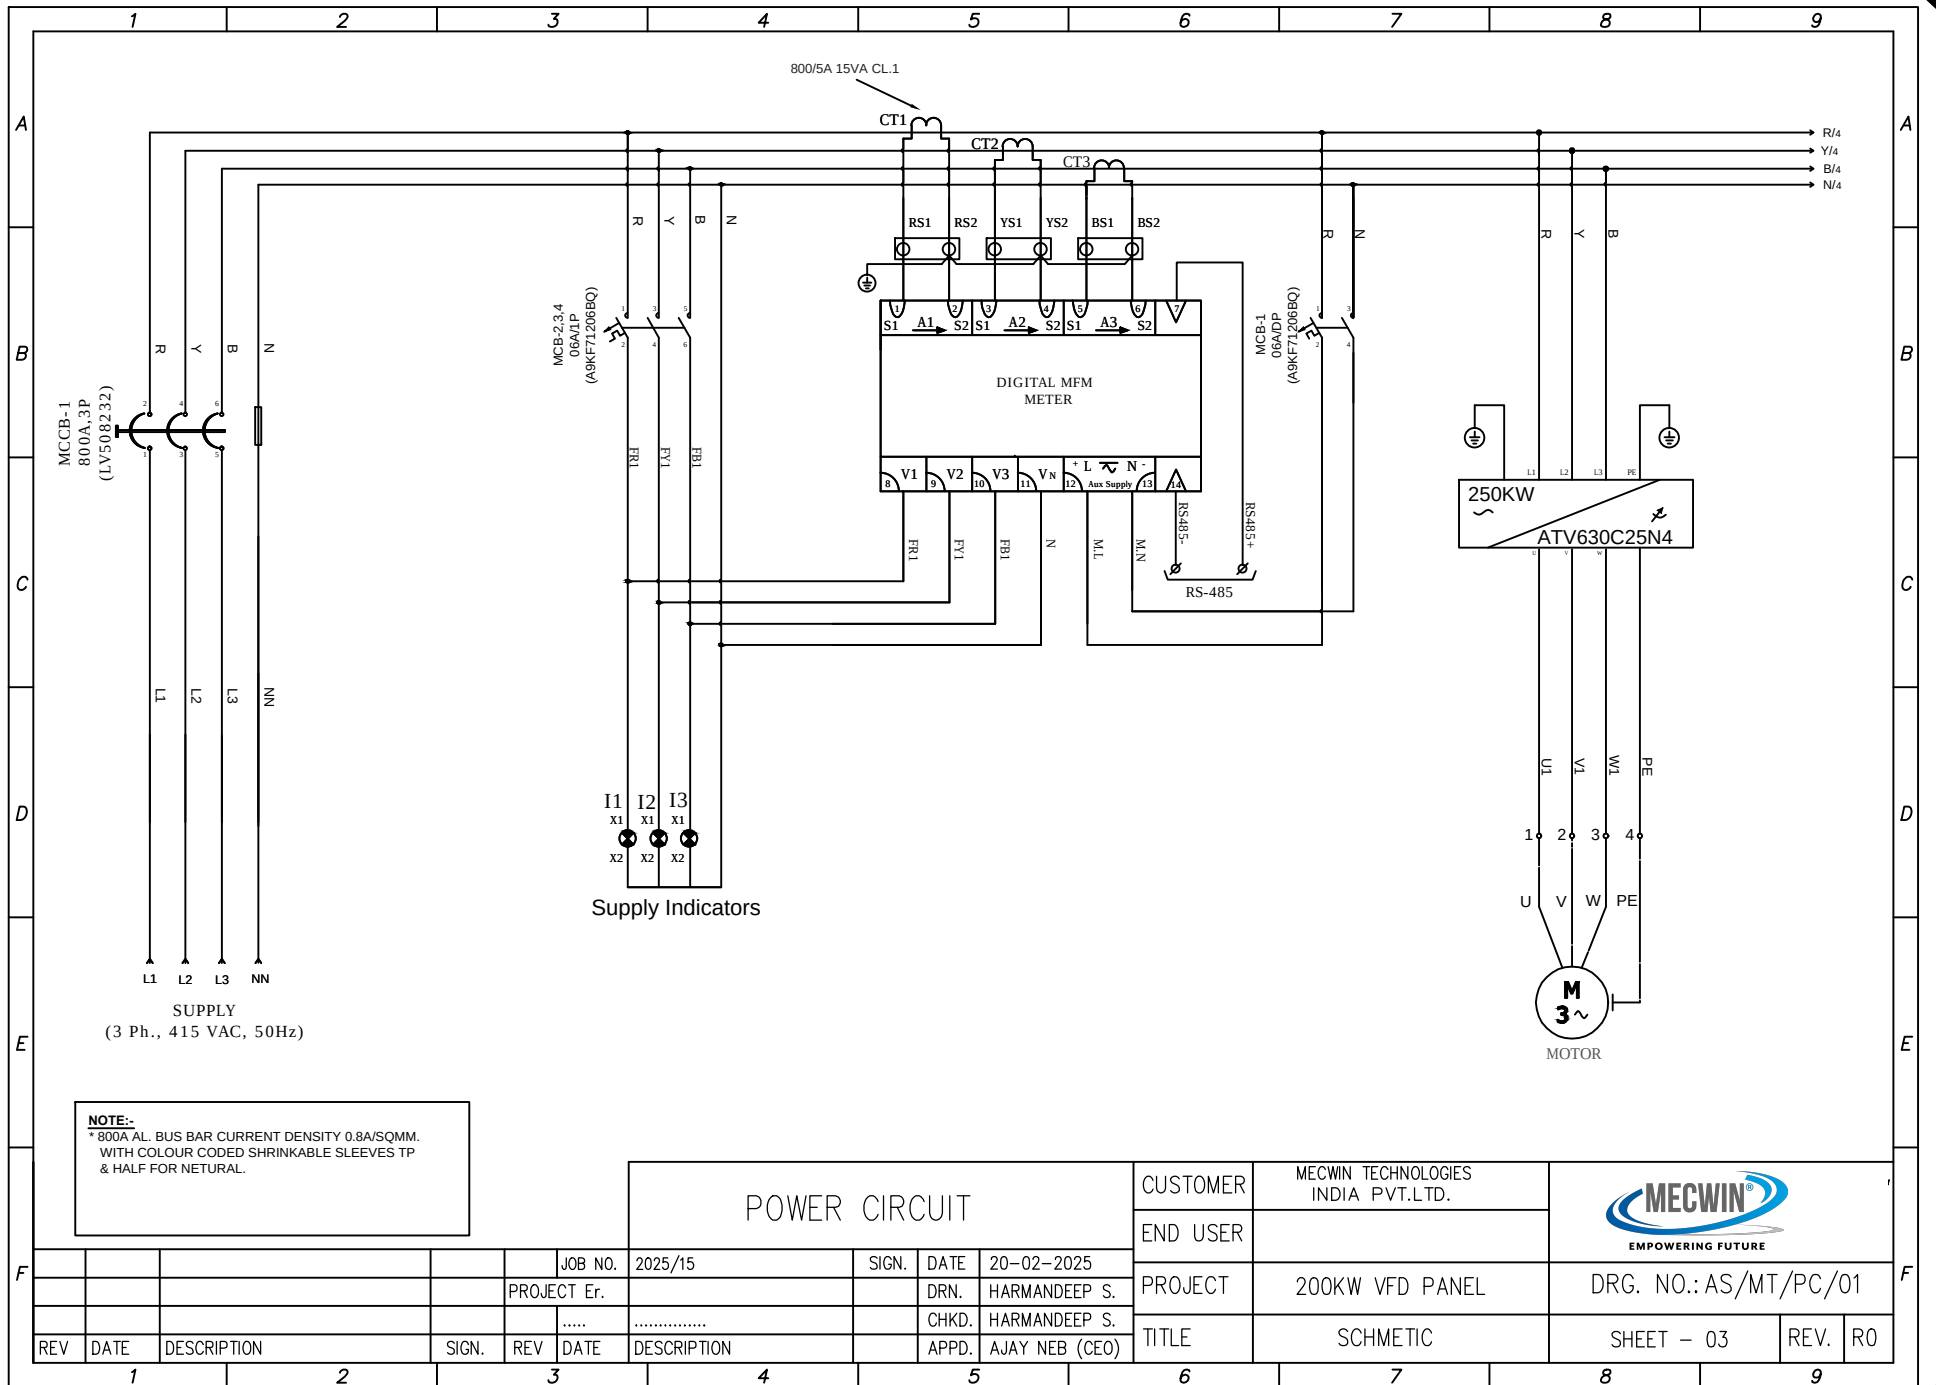

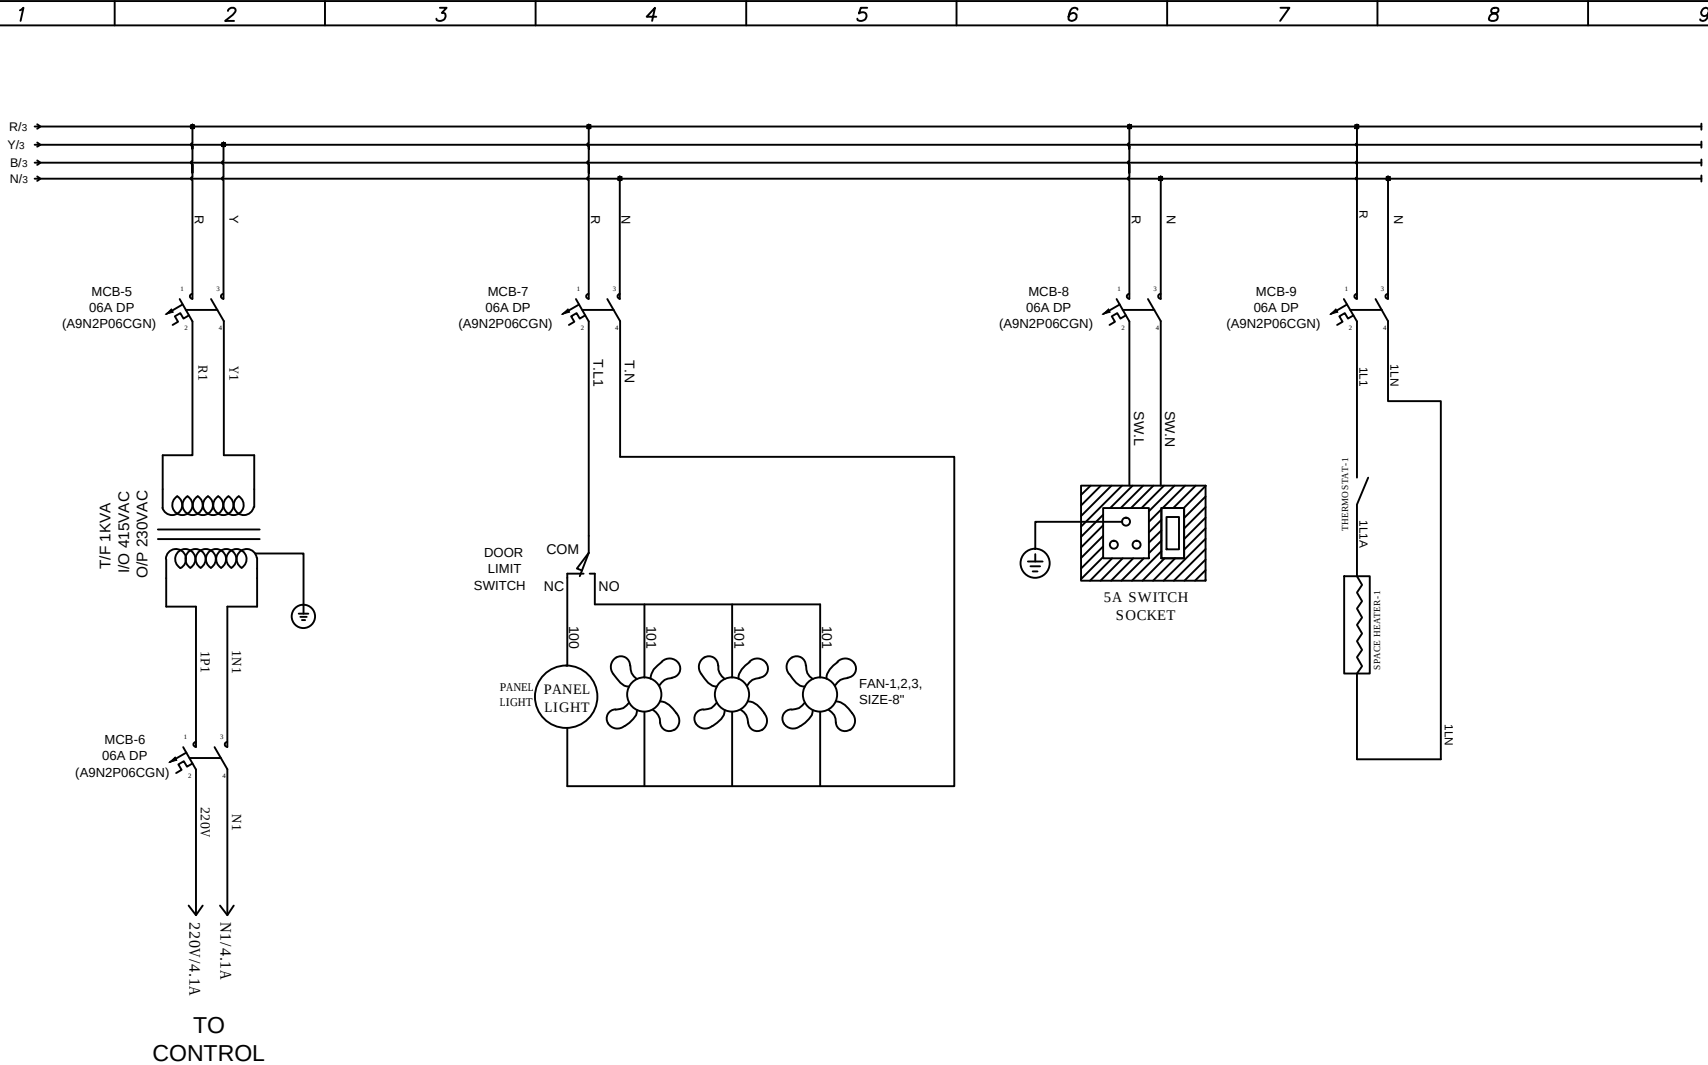

POWER CIRCUIT

CUSTOMER	MECWIN TECHNOLOGIES INDIA PVT.LTD.			
END USER				
PROJECT	200KW VFD PANEL	DRG. NO.: AS/MT/PC/02		
TITLE	SCHMETIC	SHEET – 04	REV.	R0

JOB NO.		2025/15		SIGN.		DATE		20-02-2025	
PROJECT		Er.		DRN.		HARMADEEP S.		CHKD.	
.....				APPD.		AJAY NEB (CEO)			
REV	DATE	DESCRIPTION		SIGN.	REV	DATE	DESCRIPTION		